


PLANE TABLE SURVEY

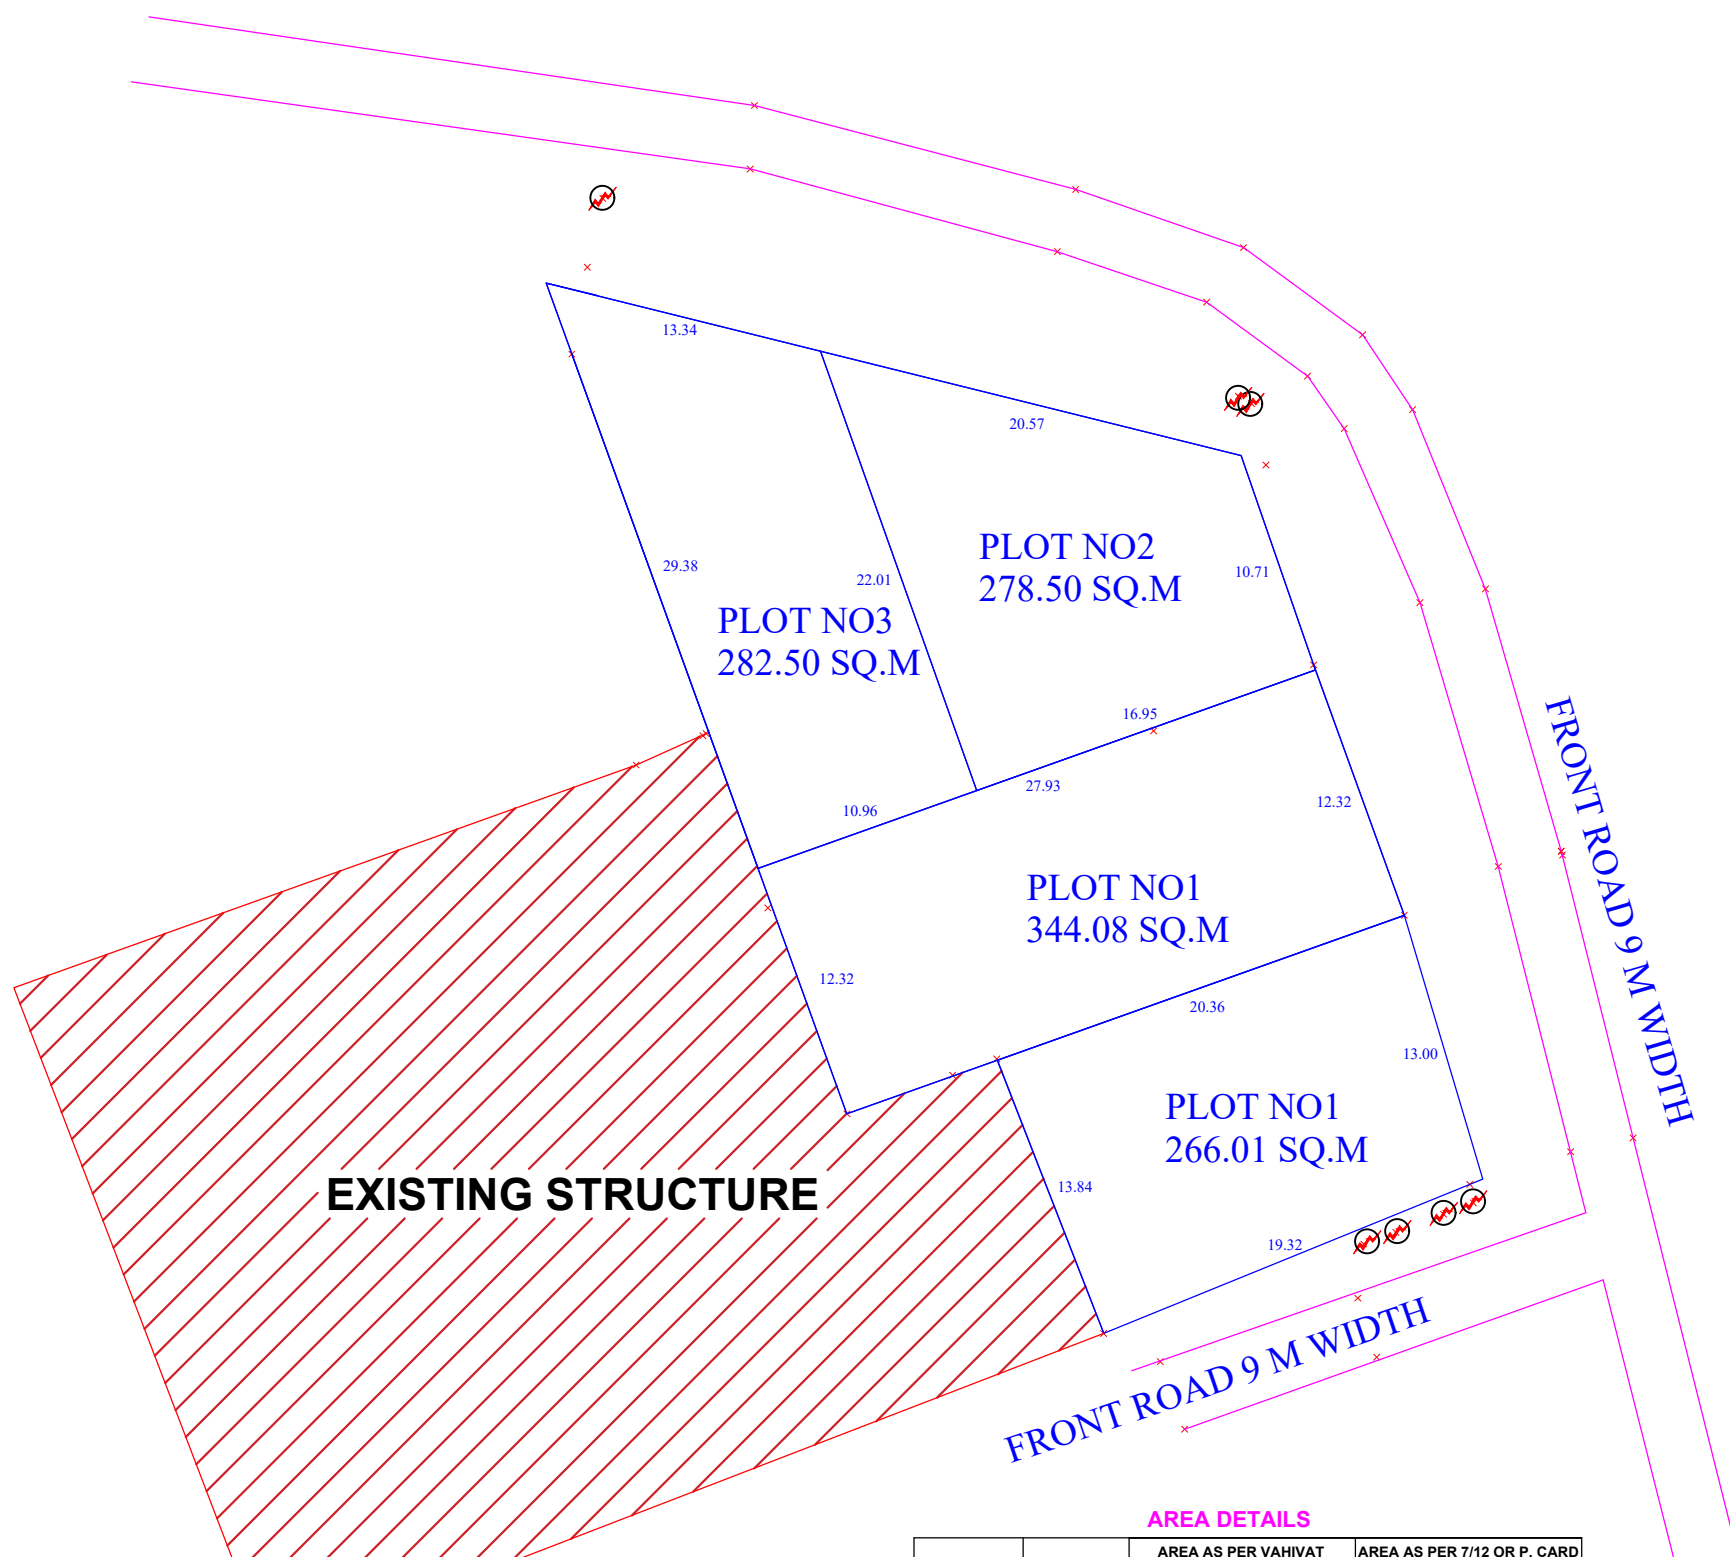

AREA DETAILS					
SR.NO	PLOT NO	AREA AS PER VAHIVAT		AREA AS PER 7/12 OR P. CARD	
		IN SQ.MTR.	IN SQ.FT.	IN SQ.MTR.	IN SQ.FT.
140/2/1/A	PLOT NO 1	344.08	3702.30	344.00	3701.44
140/2/1/A	PLOT NO 2	278.50	2996.66	278.50	2996.66
140/2/1/A	PLOT NO 3	282.50	3039.70	282.50	3039.70
140/2/1/A	PLOT NO 1	266.01	2862.26	266.00	2862.16
		1171.09	12600.92	1171.09	12599.96

LEGENDS

MAN HOLE		METALLED ROAD CARPET		NALLA / WATER LINE	
BORE WELL		UNMETALLED ROAD WAY		O.F.C. STONE	
TANK / LAKE		FIXED STONES BY T.I.L.R.		KILOMETER STONE	
CONTOUR		CONCRETE POLE ON SITE		RAILWAY LINE	
ELECTRIC POLE		GARDEN / LAWN		H.T. LINE	
TELEPHONE POLE		TEMPRORY STRUCTURE		UNDERGROUND PIPE	
FENCING LINES & COMPOUND WALL		PERMENENT STRUCTURE		COCONUT TREE	
BENCH MARKS		BRIDGE / CULVERTS		OTHER TREES	
STATION MARKS		GUTTER / SMALL FLOWS		AS PER VAHIVAT	
LAMP POST		PLOT BOUNDRY AS PER VAHIVAT			
ENTRANCE GATE		PLOT BOUNDRY AS PER T.I.L.R. MAP			

STATION LIST

STN	EAST	NORTH	ELEV.	STN	EAST	NORTH	ELEV.
ST 1				ST 3			
ST 2				ST 4			

SITE ON GOOGLE EARTH :

AREA DETAILS

AREA AS PER VAHIVAT		AREA AS PER 7/12 OR P. CARD	
IN SQ.MTR.	IN SQ.FT.	IN SQ.MTR.	IN SQ.FT.
CLOSED TRAVERSE SYMBOLS		AREA UNDER ACQUISITION	
A - B - C - D - E			
PERIMETER	-----MTR.		

ALL DIMENSIONS ARE IN METER

PURPOSE OF ISSUE			
TENDER	☐	INFORMATION	☒
REVIEW / APPROVAL	☐	CONSTRUCTION	☐
AS-BUILT	☐		
PROJECT NAME : PLANE TABLE SURVEY			
ARCHITECT :			
CLIENT NAME : RAJU MORE			
DRN.	SIGN	DATE	
CHKD.			
APPD.			
UNLESS OTHERWISE STATED ALL DIMENSIONS ARE IN Mtr.			
TITLE: PLANE TABLE SURVEY			
SITE ON GOOGLE EARTH :			
GEOMAPS SURVEYORS			
Mo.No - 9561491312			
SCALE			CAD FILE
1:100			
DRAWING NO.			REV.
			I
SHEET NO.			NO. OF SH.